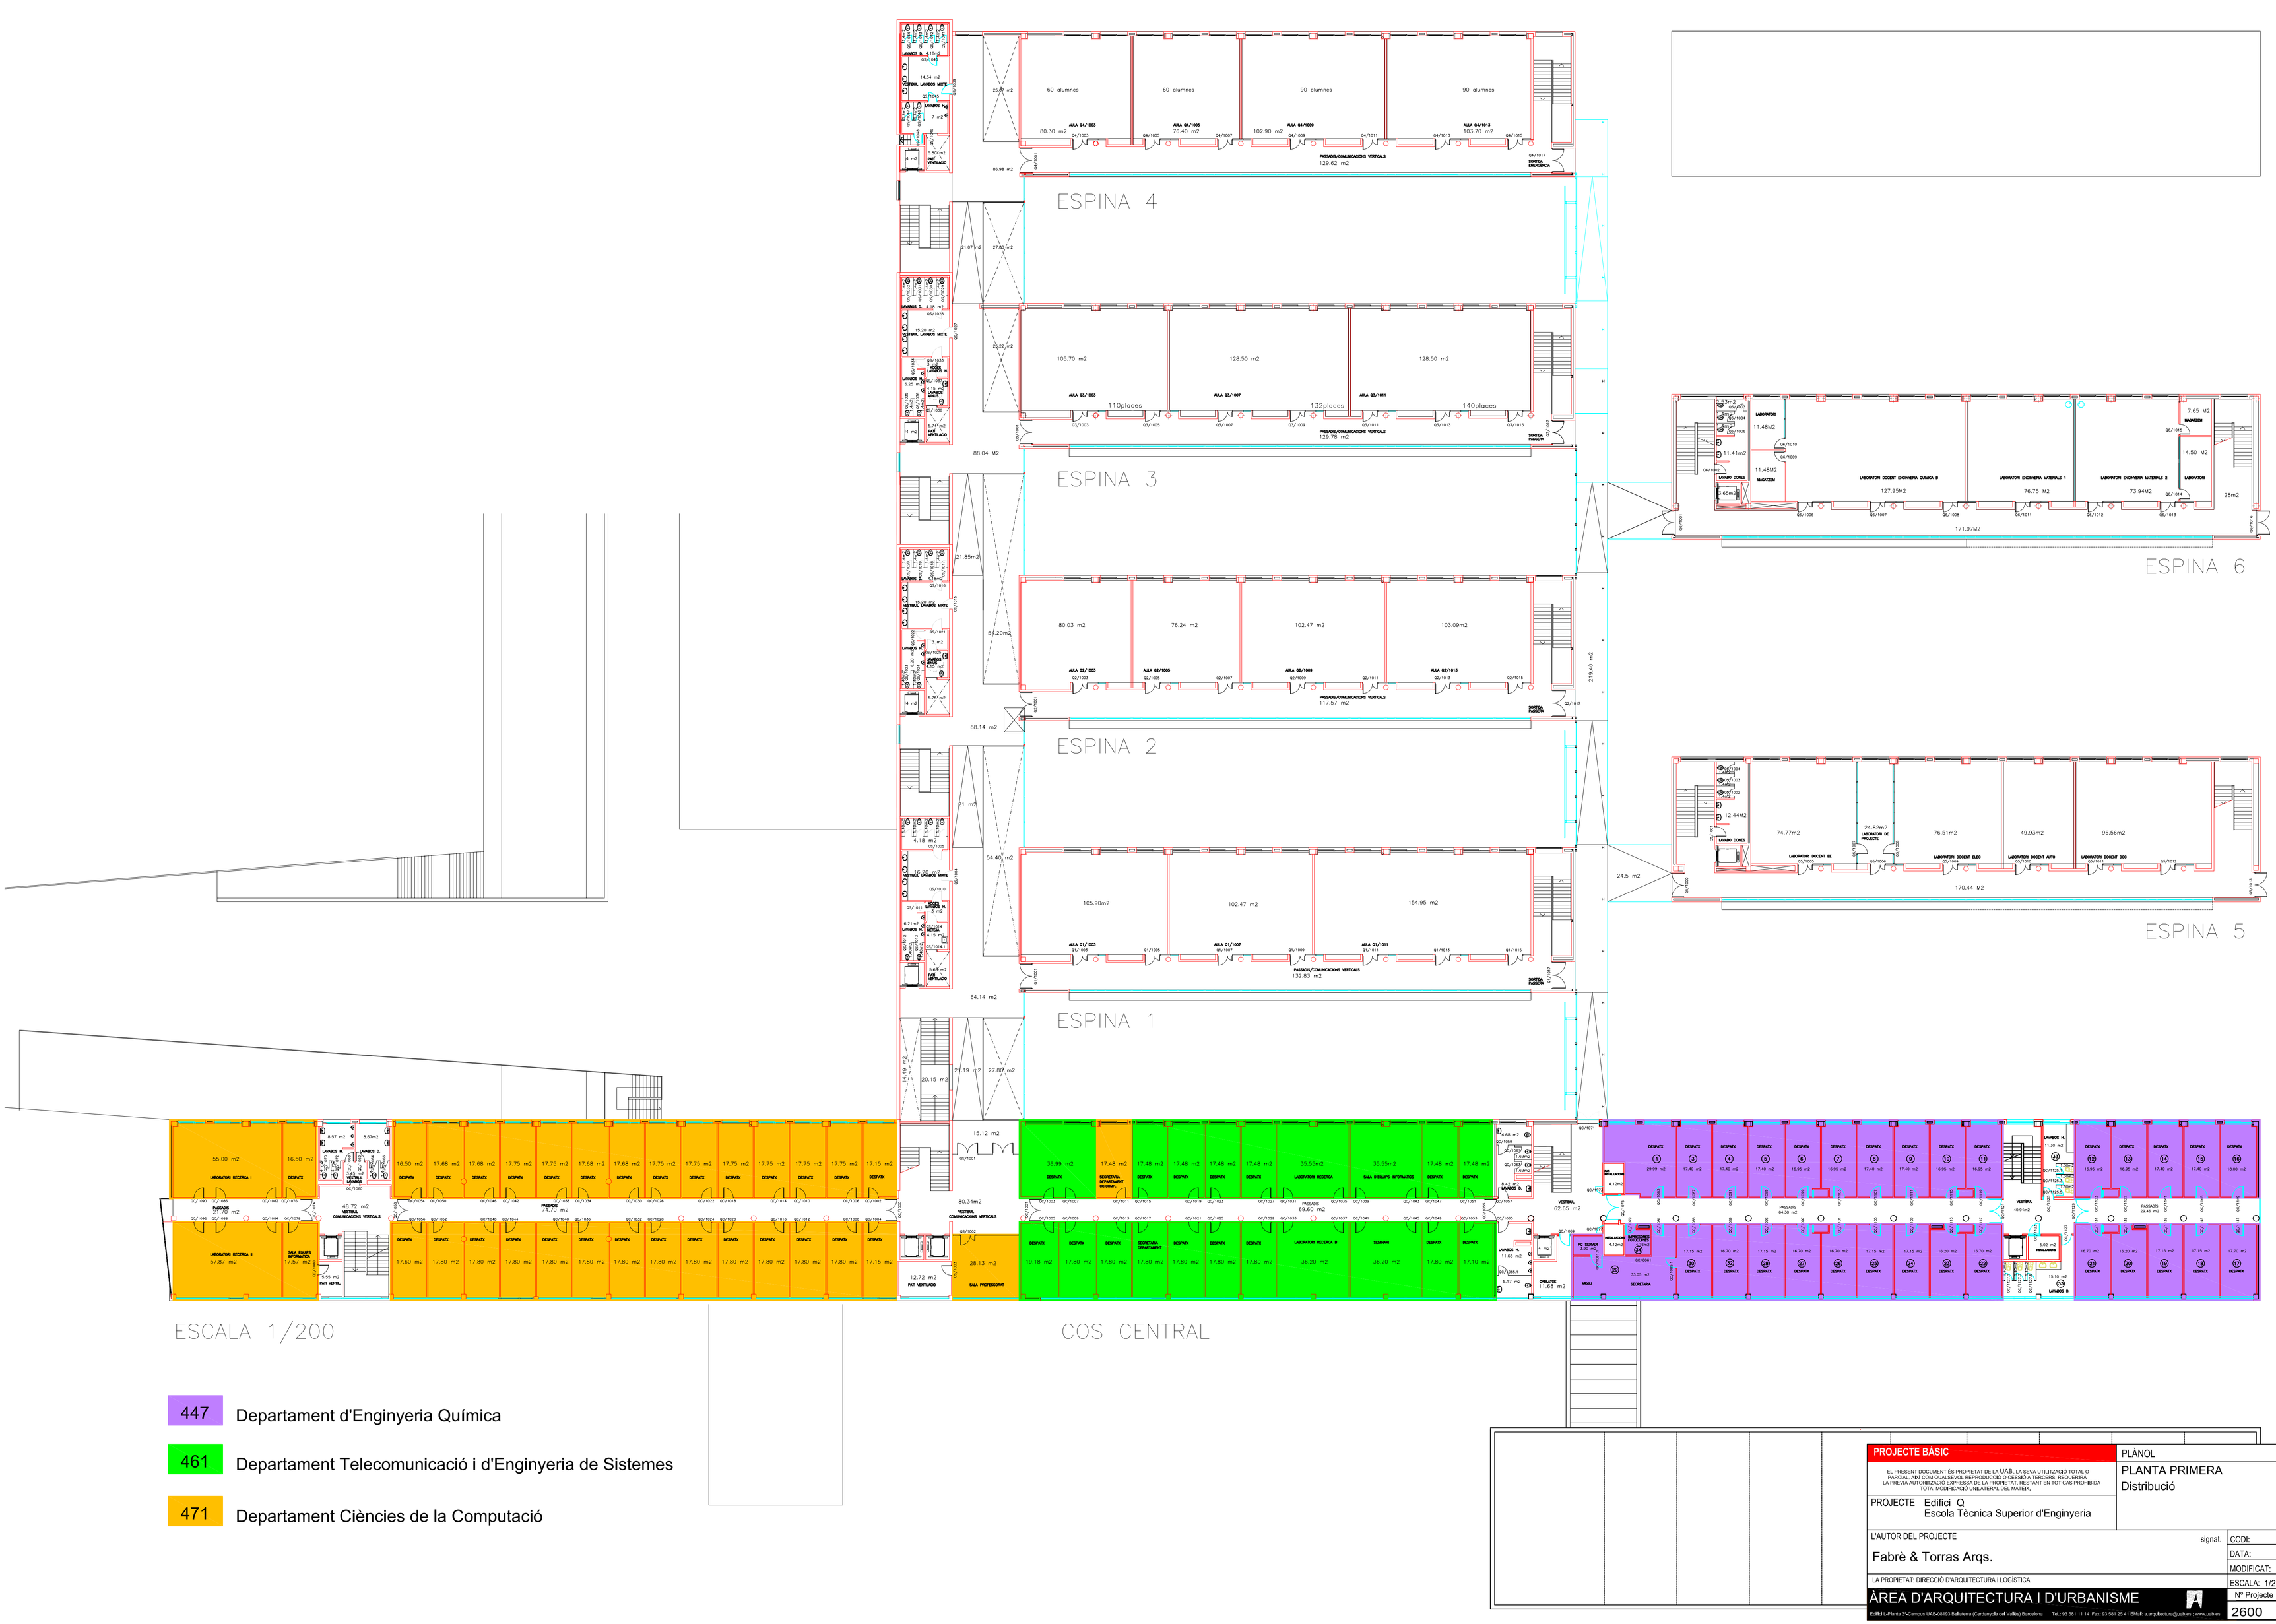


PROJECTE BÀSIC

EL PRESENT DOCUMENT ÉS PROPIETAT DE LA UAB. LA SEVA UTILITZACIÓ TOTAL O PARCIAL, AMB CUALSEVOL SUPORT, REPRODUCCIÓ O CESSIÓ A TERCERS, REQUERIRÀ LA PREVIA AUTORITZACIÓ ESCRITA DE LA PROPIETAT, RESTANT EN TOT CAS PROHIBIDA TOTA MODIFICACIÓ UNILATERAL DEL MATEIX.

PROJECTE Edifici O
Escola Tècnica Superior d'Enginyeria

L'AUTOR DEL PROJECTE

Fabrè & Torras Arqs.

signat.

LA PROPIETAT: DIRECCIÓ D'ARQUITECTURA I LOGÍSTICA

ÀREA D'ARQUITECTURA I D'URBANISME

Edifici La Penta (Pl.Campus UAB)-08193 Bellaterra (Cerdanyola del Vallès) Barcelona Tel.(93 581 11 14 Fax) 93 581 25 41 EMail: a.arq.arquitectura@uab.es / www.uab.es

PLÀNOL

PLANTA PRIMERA
Distribució

CODI:	2600.003
DATA:	08/03
MODIFICAT:	27/11/06
ESCALA: 1/250	FORMAT: A1

Nº Projecte	Capítol	Nº Plànol	V.
2600		003	