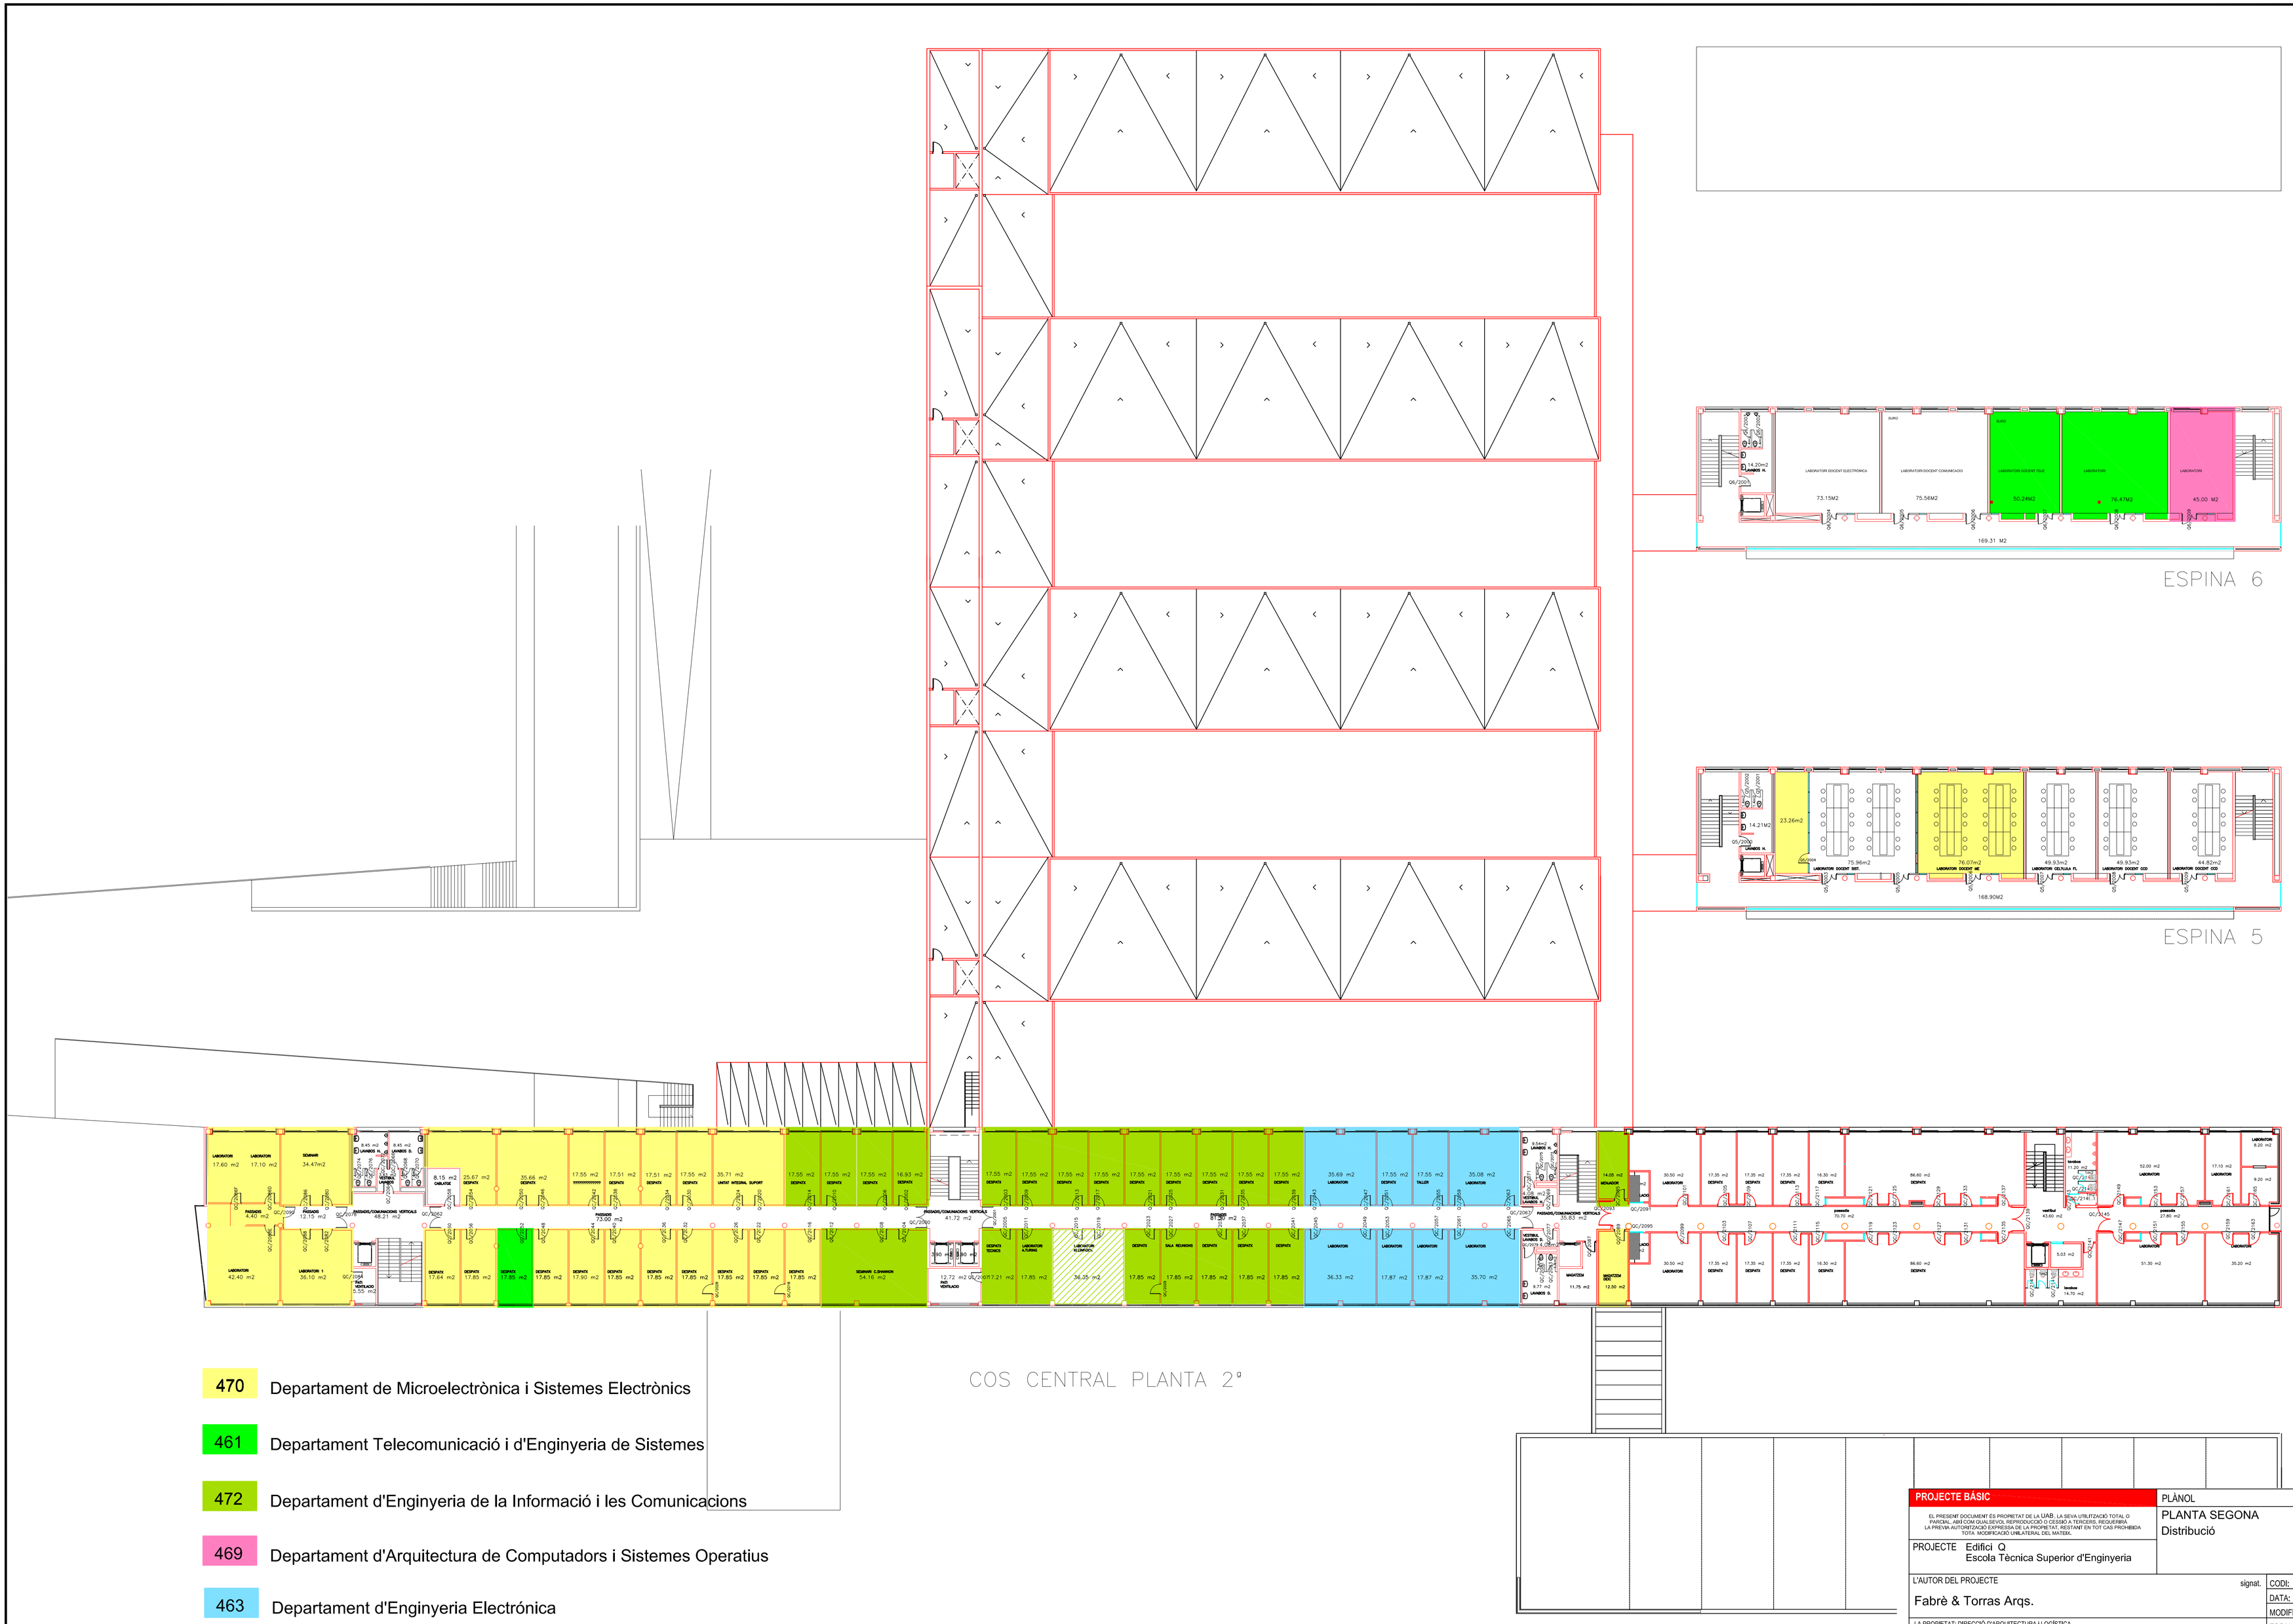


PROJECTE BÀSIC

PLÀNOL

UAB

PLANTA SEGONA
Distribució

EL PRESENT DOCUMENT ÉS PROPIETAT DE LA UAB. LA SEVA UTILITZACIÓ TOTAL O PARCIAL, AMB COM QUALSEVOL REPRODUCCIÓ O CESSIÓ A TERCERS, REQUEREIX LA PREVIA AUTORITZACIÓ EXPRESSA DE LA PROPIETAT, RESTANT EN TOT CAS PROHIBIDA TOTA MODIFICACIÓ UNILATERAL DEL MATEIX.

PROJECTE Edifici Q
Escola Tècnica Superior d'Enginyeria

L'AUTOR DEL PROJECTE
Fabrè & Torras Arqs.

signat.

LA PROPIETAT: DIRECCIÓ D'ARQUITECTURA I LOGÍSTICA

ÀREA D'ARQUITECTURA I D'URBANISME

CODI:	2600.004
DATA:	08/03/06
MODIFICAT:	03/04/08
ESCALA: 1/250	FORMAT: A1

Nº Projecte | Capítol | Nº Plànol | V.